

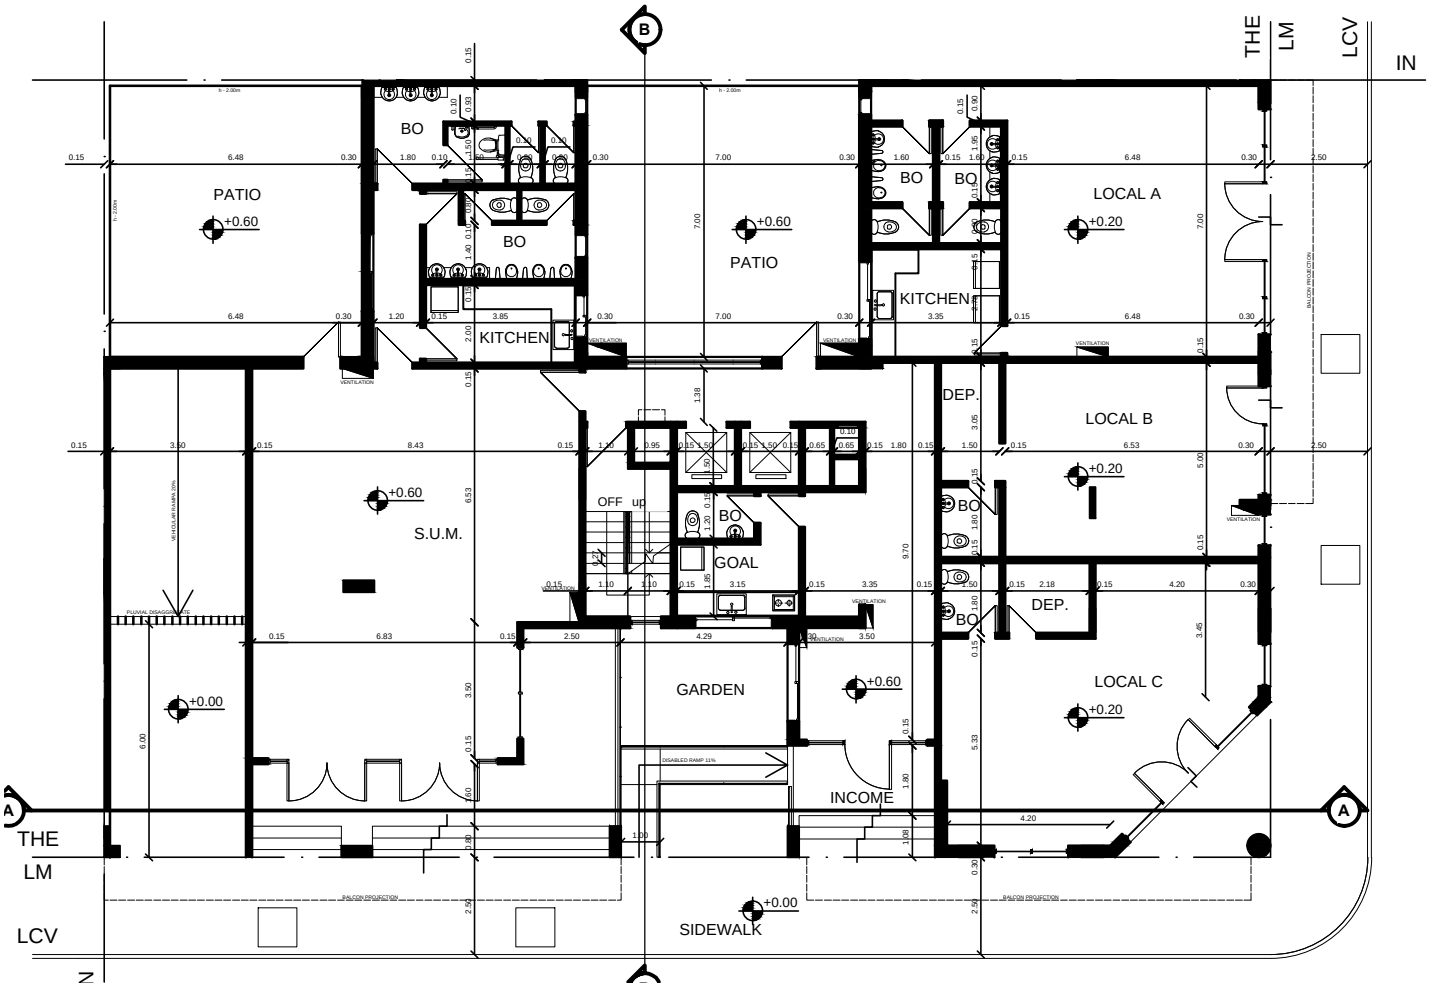


GROUND FLOOR BOUND

ESC. 1:100

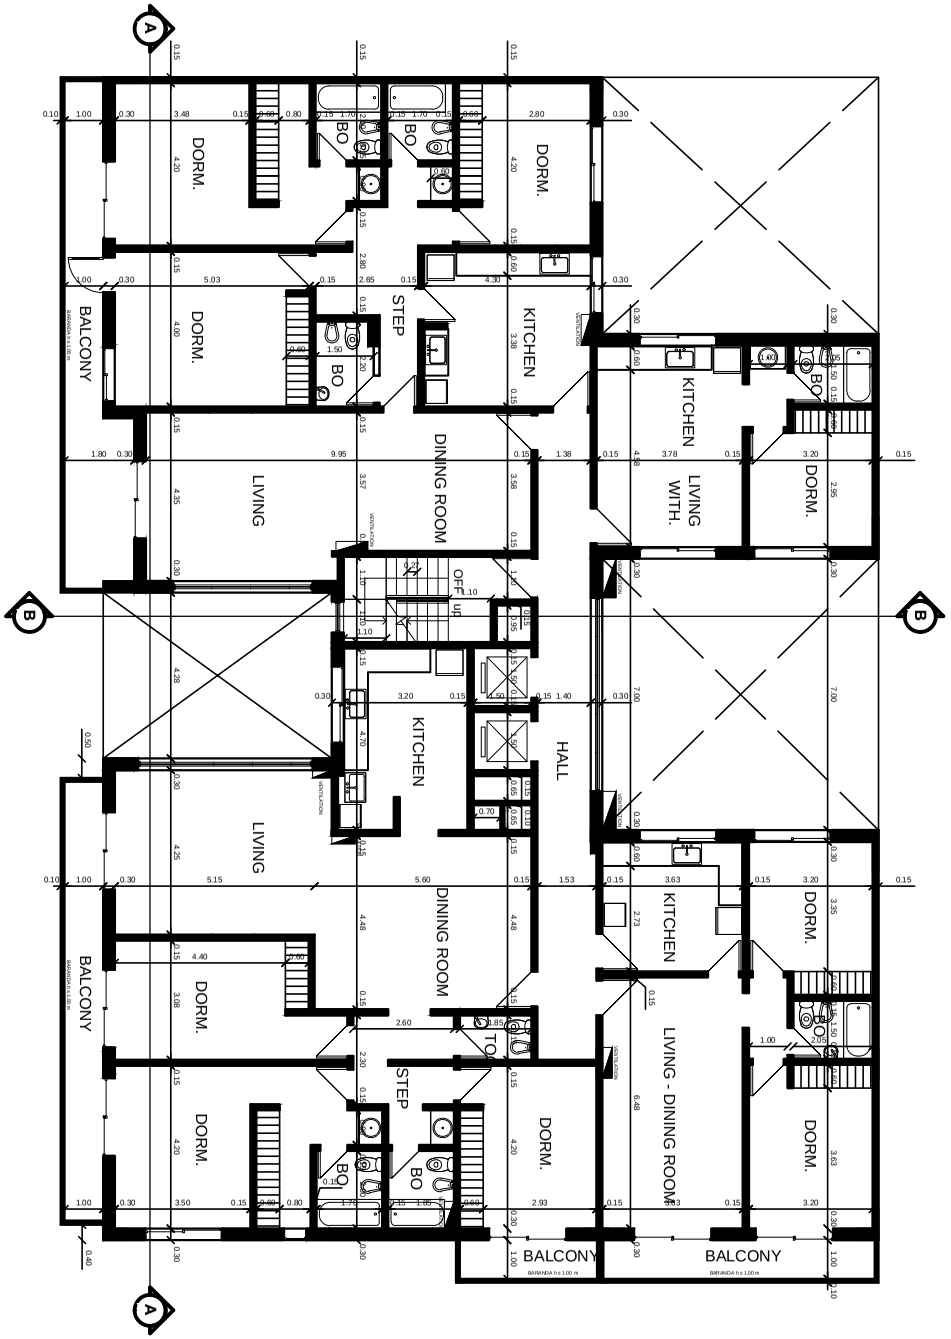



TYPE FLOOR 1st and 2nd FLOOR ACOTADA ES

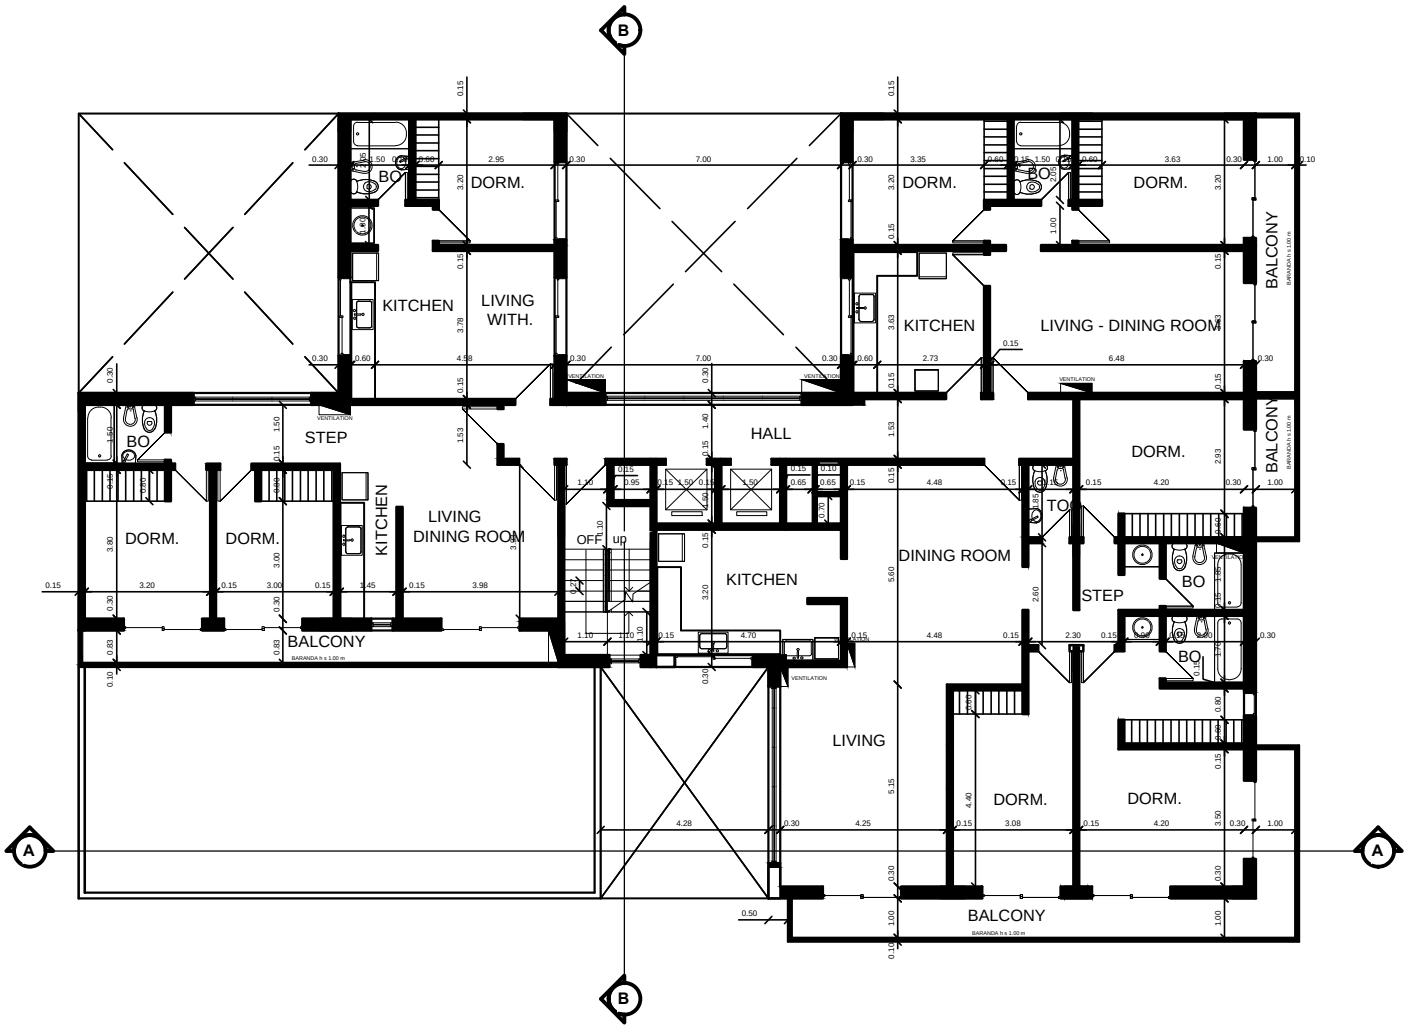


TYPE FLOOR 3rd and 6th FLOOR LIMITED ESC.

ROOF
ESC. 1:100

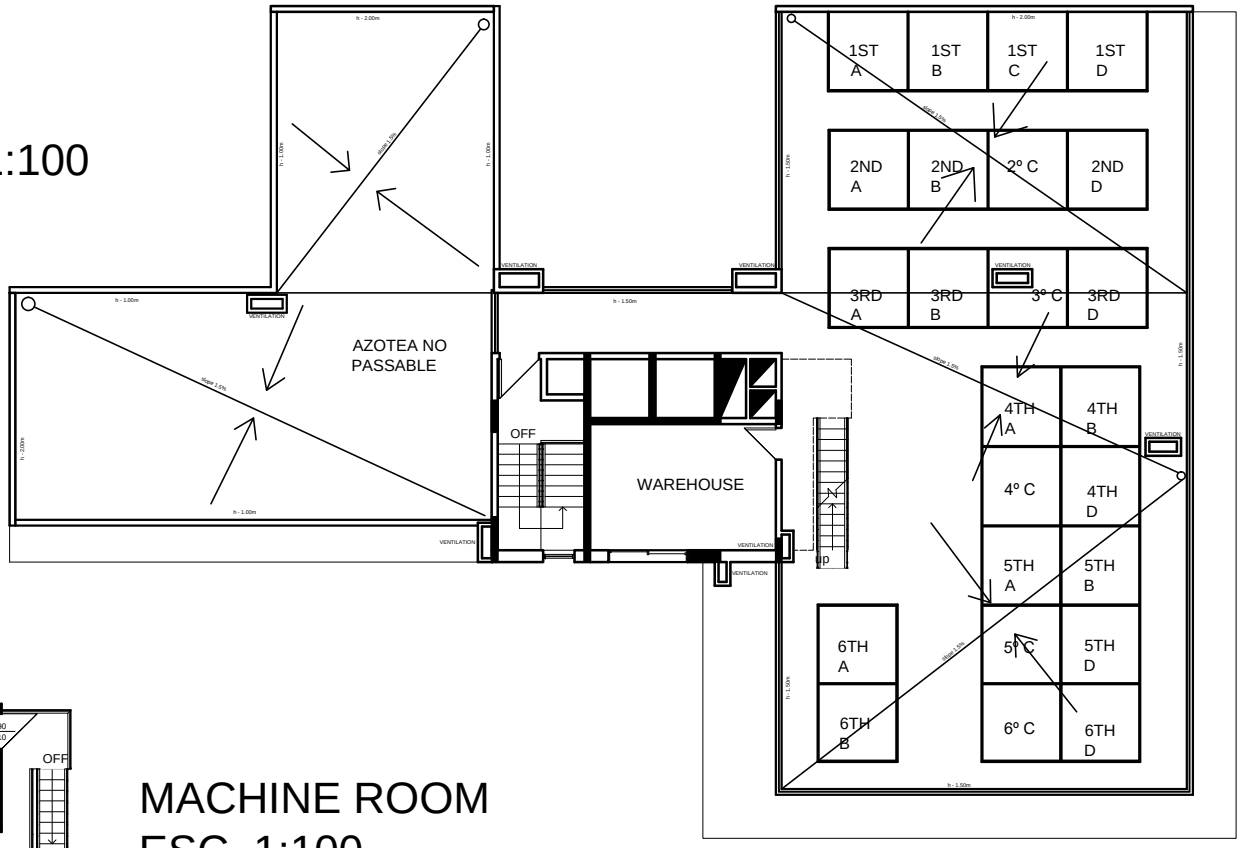


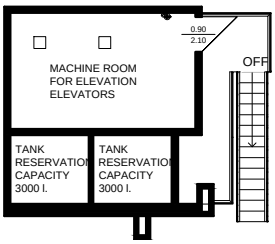


MACHINE ROOM
ESC. 1:100

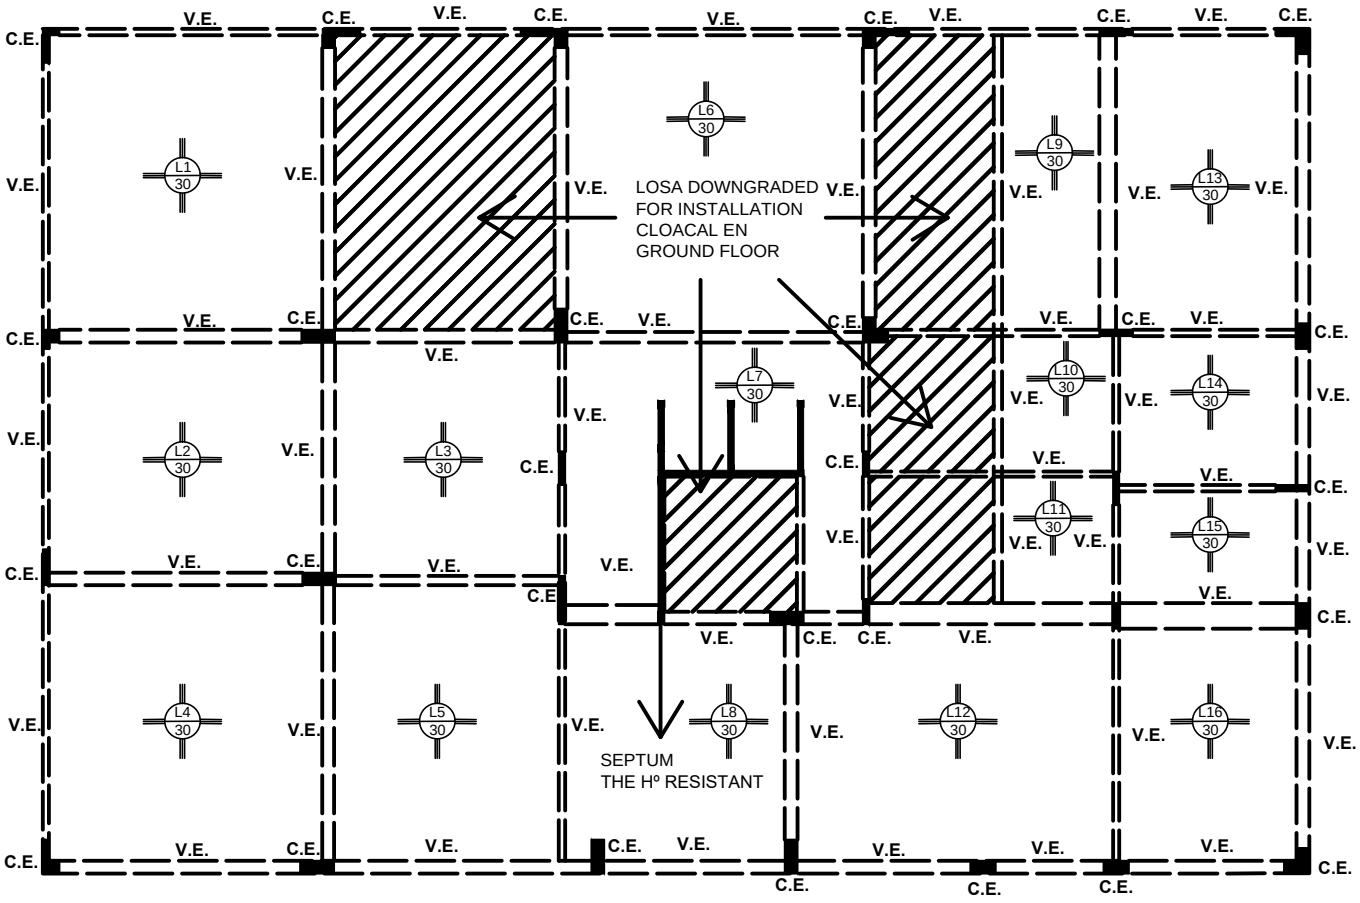
LOSA DOWNGRADED
FOR INSTALLATION
CLOACAL EN
GROUND FLOOR
SEPTUM
THE Hº RESISTANT
L1 30
L2 30
L3 30
L4 30
L5 30
L6 30
L7 30
L8 30
L9 30
L10 30
L11 30
L12 30
L13 30
L14 30
L15 30
L16 30
V.E.
C.E.


pb

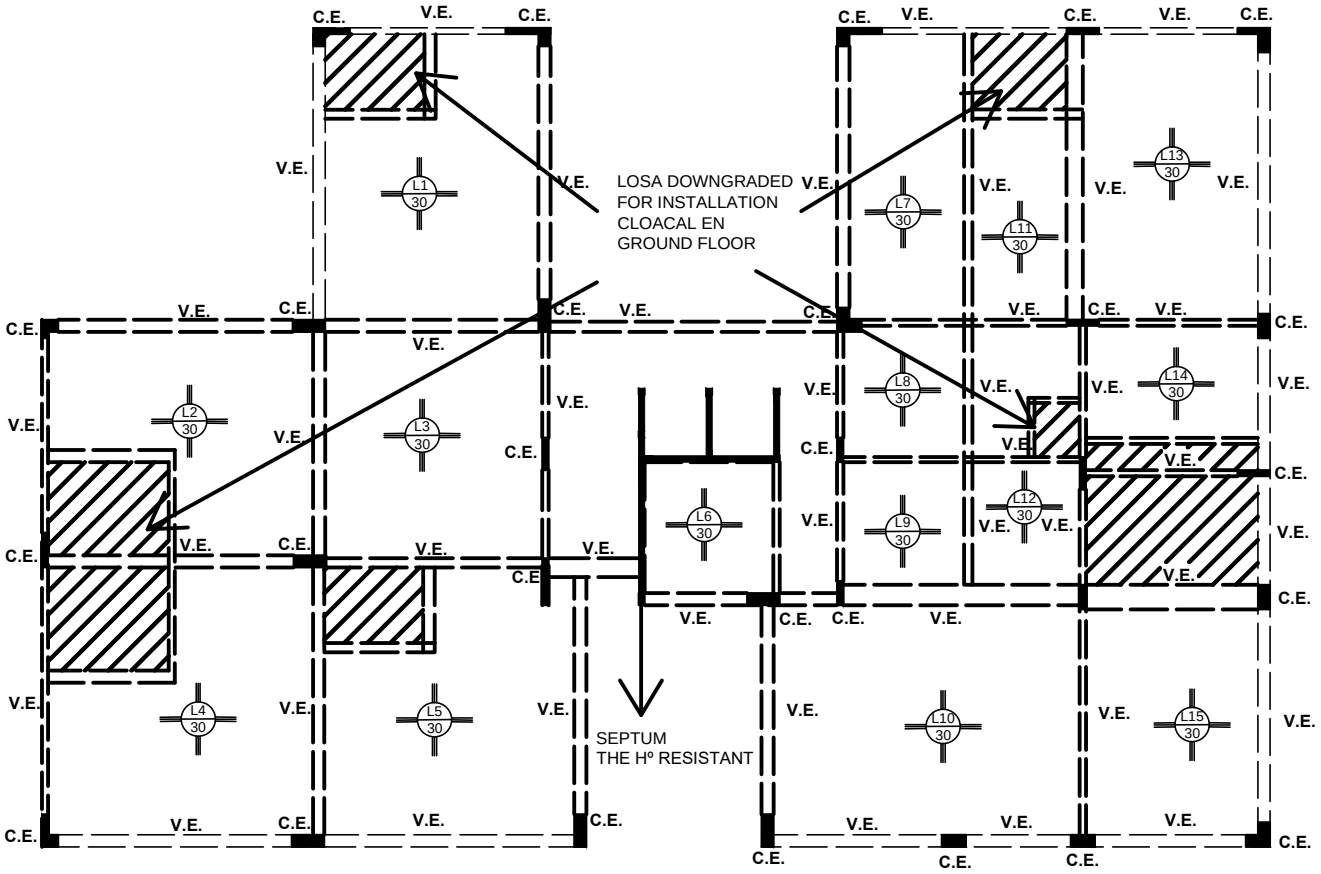


STRUCTURE FLOOR 1st and 2nd P ESC. 1:100

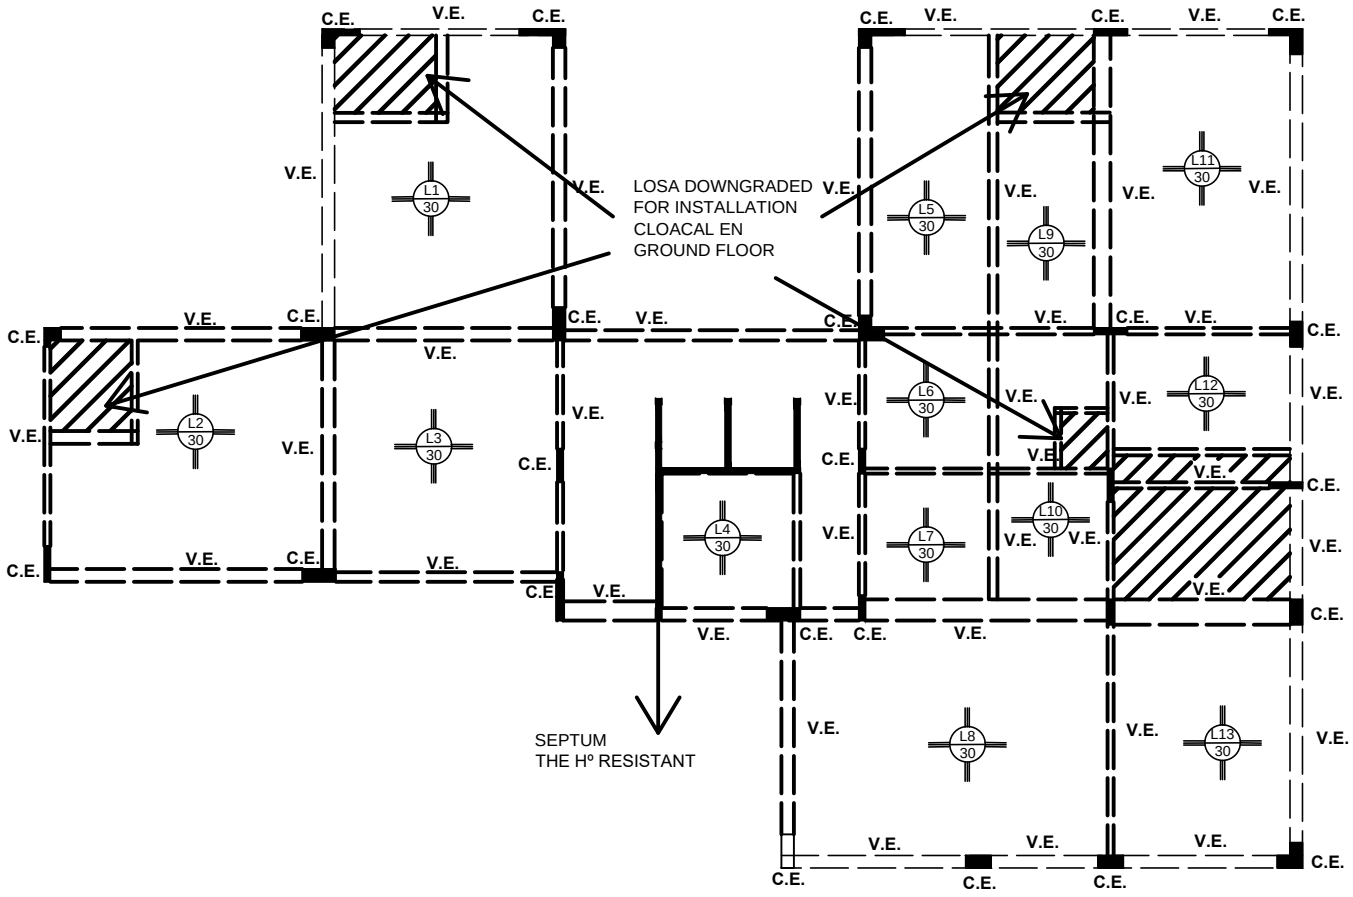


STRUCTURE FLOOR 3rd to 6th P ESC. 1:100

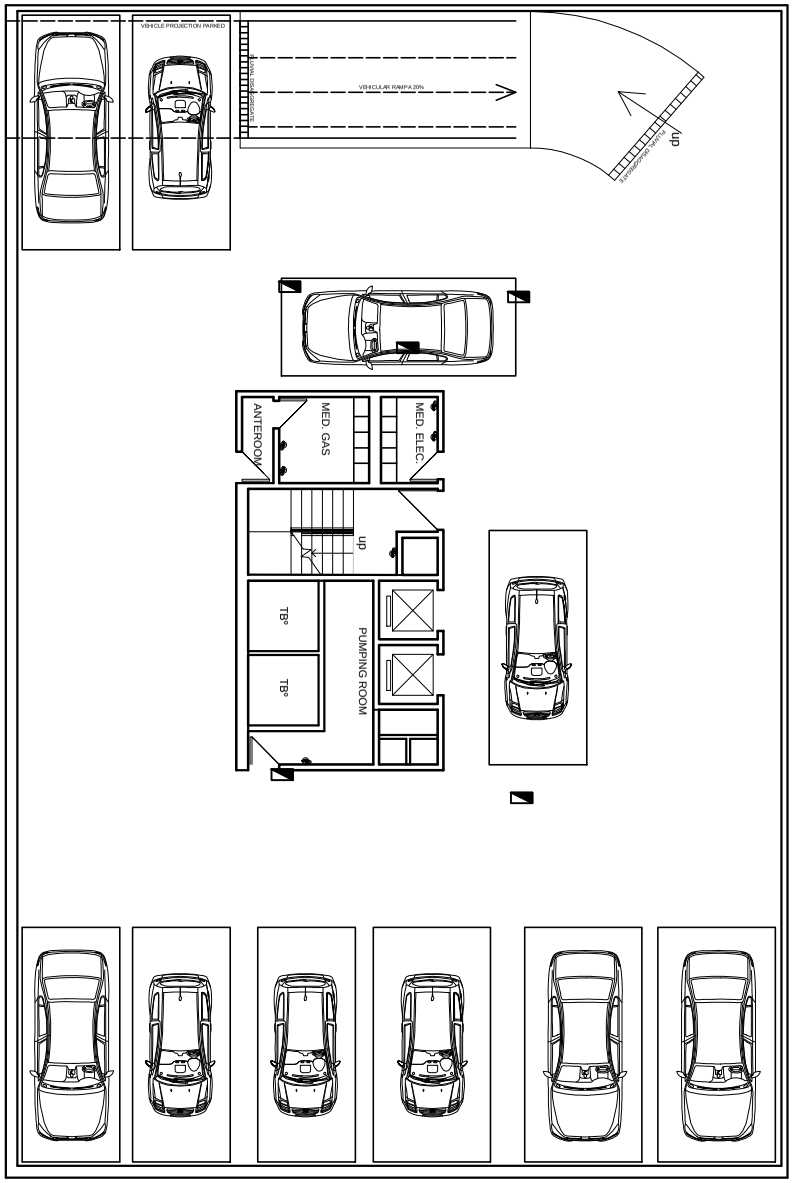

SUBSUELO - GARAGES ESC. 1:100

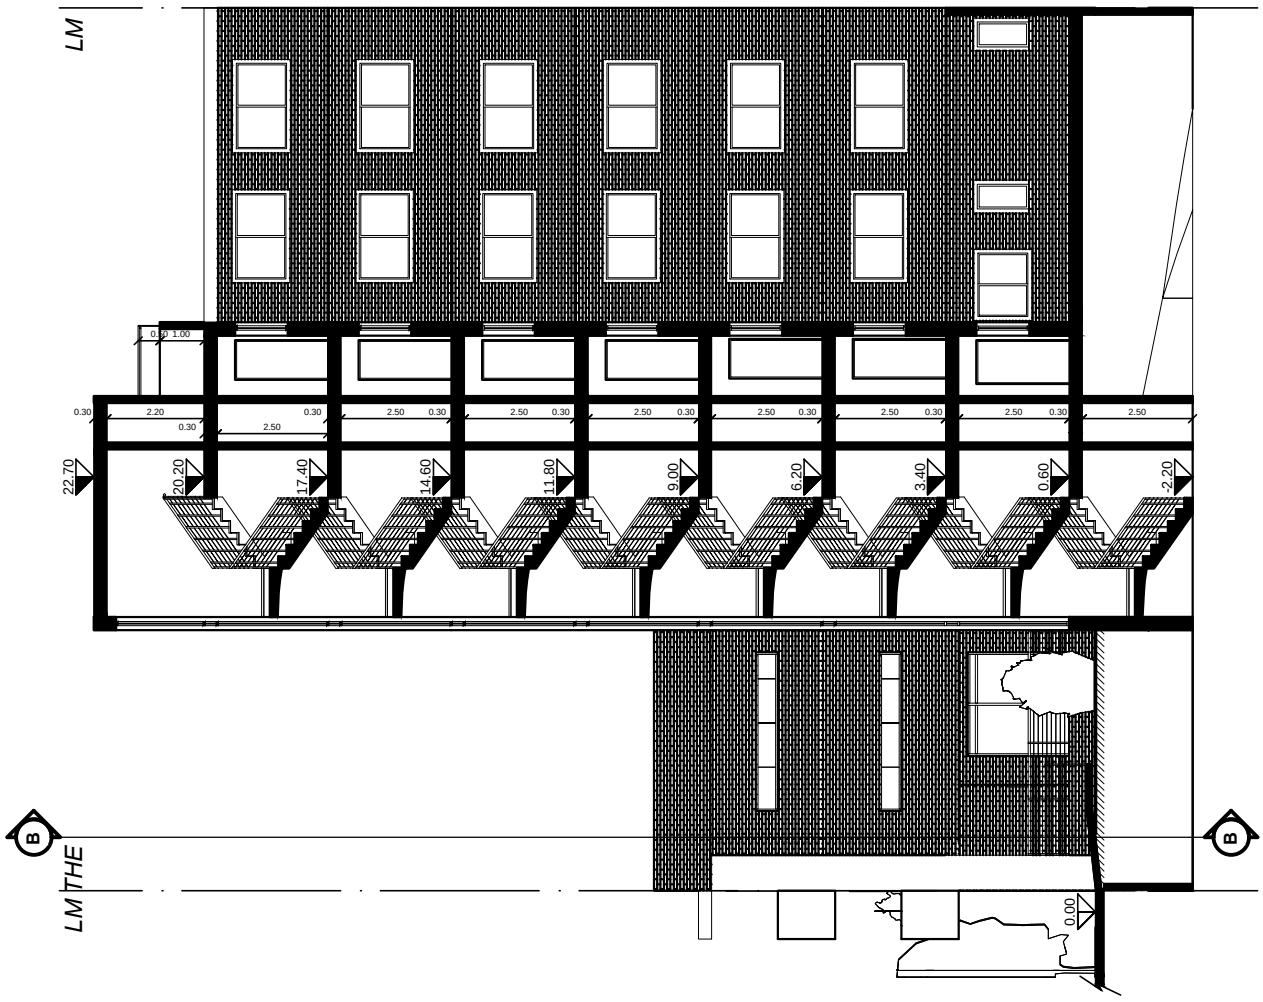

BB CUT ESC. 1:100

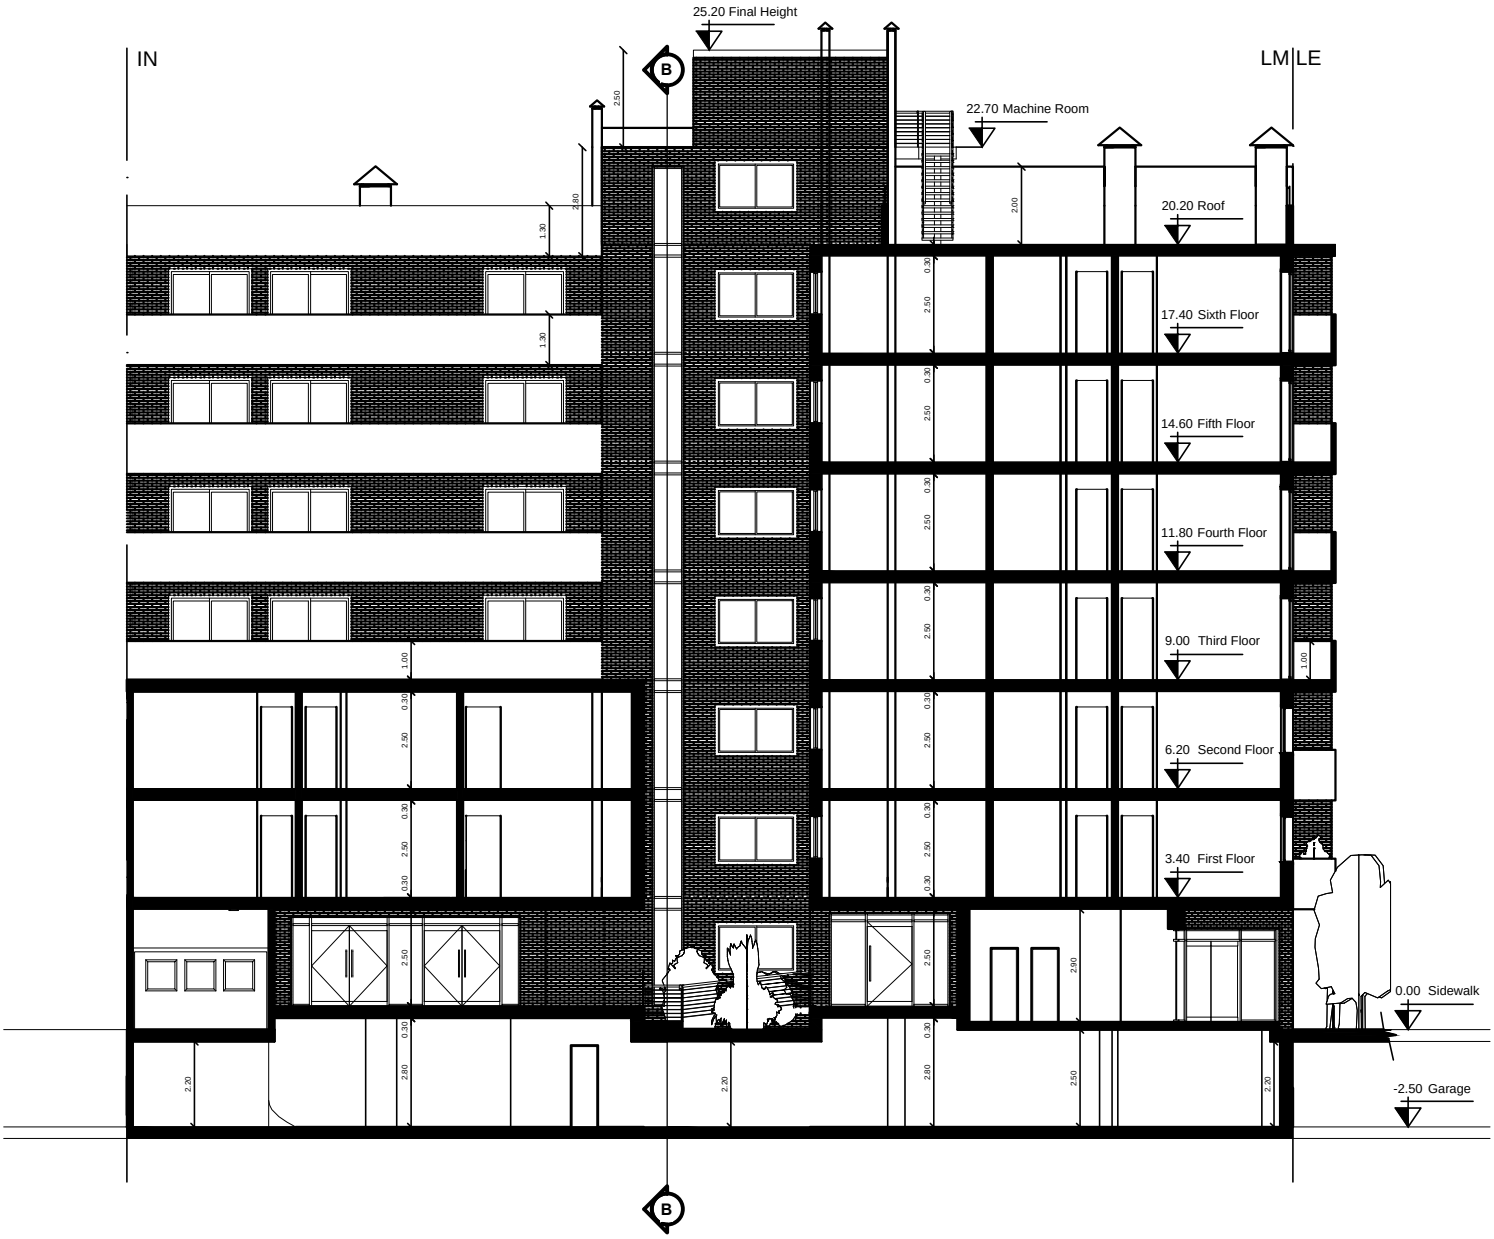

CUT AA ESC. 1:100